


OCIEPLENIE STANDARD

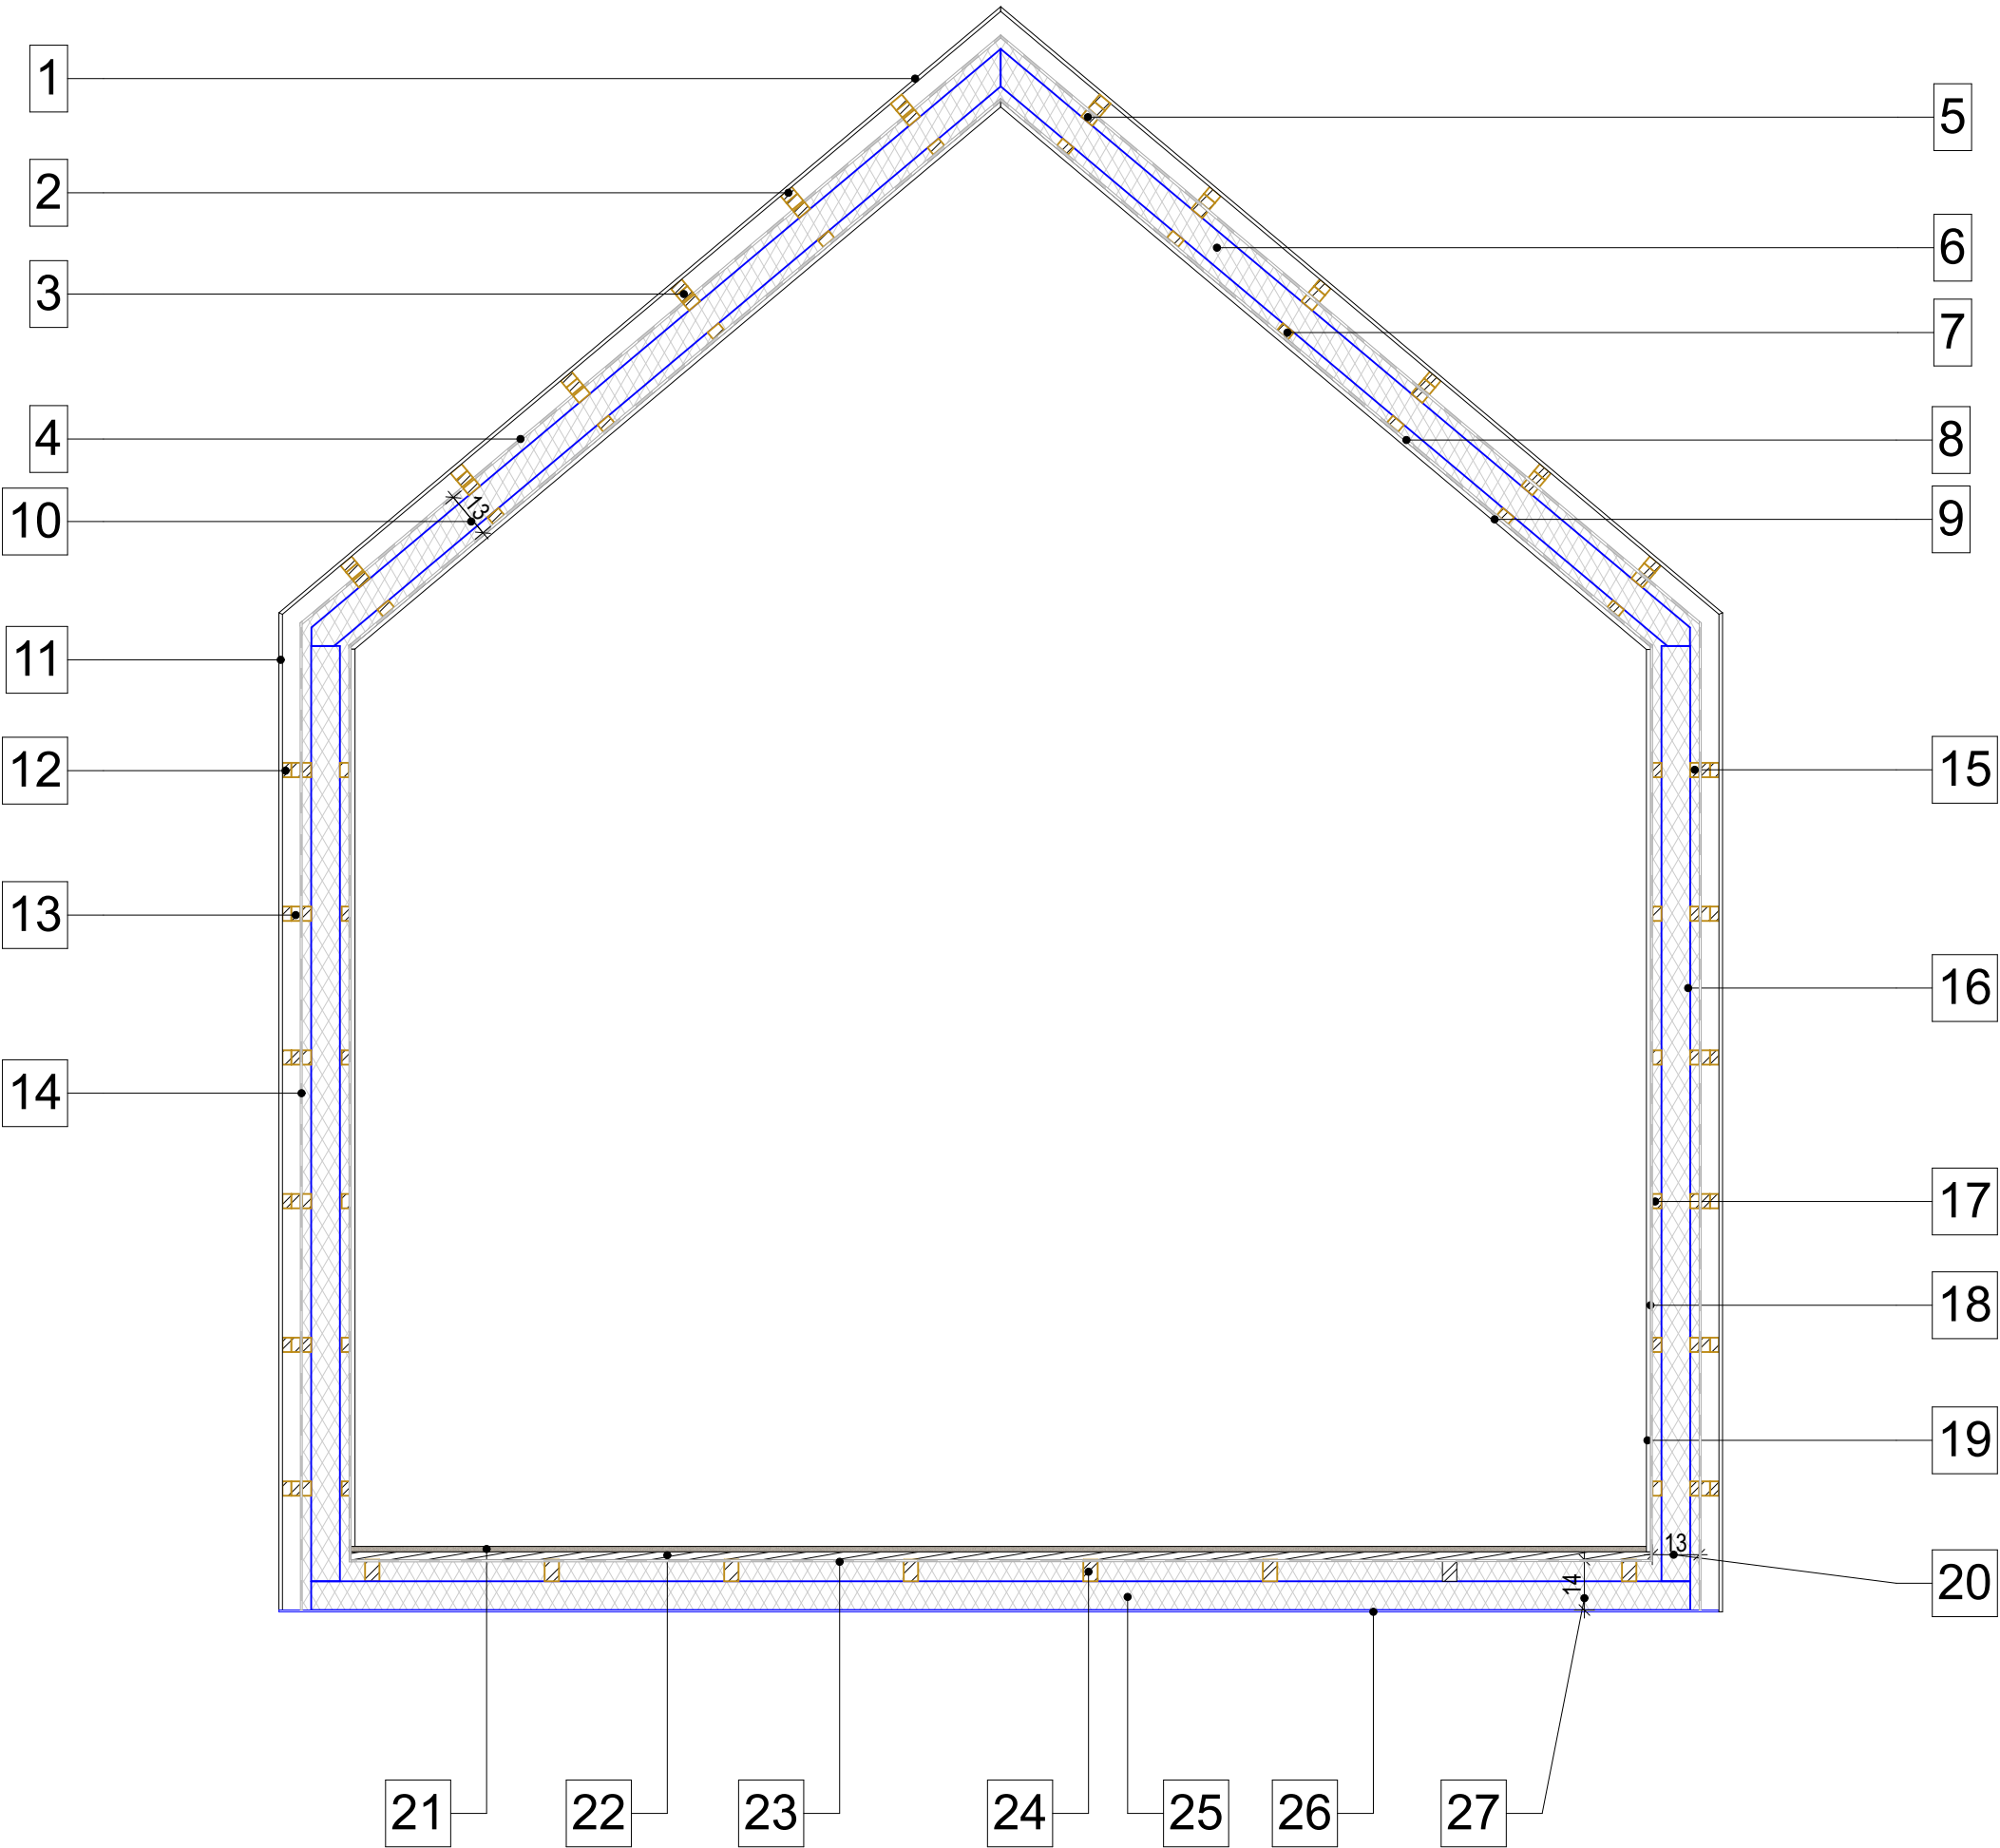

DACH		
1	BLACHA NA RĄBEK	25MM
2	KONTRŁATA POZIOMA	25MM
3	KONTRŁATA PIONOWA	25MM
4	MEMBRANA	
5	KONTRŁATA PIONOWA	25MM
6	PROFIL STALOWY	80MM
7	KONTRŁATA POZIOMA	25MM
8	FOLIA PAROSZCZELNA	
9	PŁYTA STRAMA	12MM
10	IZOLACJA TERMICZNA DACHU	130MM
ŚCIANA		
11	BLACHA NA RĄBEK	25MM
12	KONTRŁATA POZIOMA	25MM
13	KONTRŁATA PIONOWA	25MM
14	MEMBRANA	
15	KONTRŁATA PIONOWA	25MM
16	PROFIL STALOWY	80MM
17	KONTRŁATA POZIOMA	25MM
18	FOLIA PAROSZCZELNA	
19	PŁYTA STRAMA	12MM
20	IZOLACJA TERMICZNA ŚCIANY	130MM
PODŁOGA		
21	PANEL	15MM
22	OSB	22MM
23	FOLIA PAROSZCZELNA	
24	ŁATA	60MM
25	PROFIL STALOWY	80MM
26	BLACHA OCYNK	0,5MM
27	IZOLACJA TERMICZNA PODŁOGI	140MM